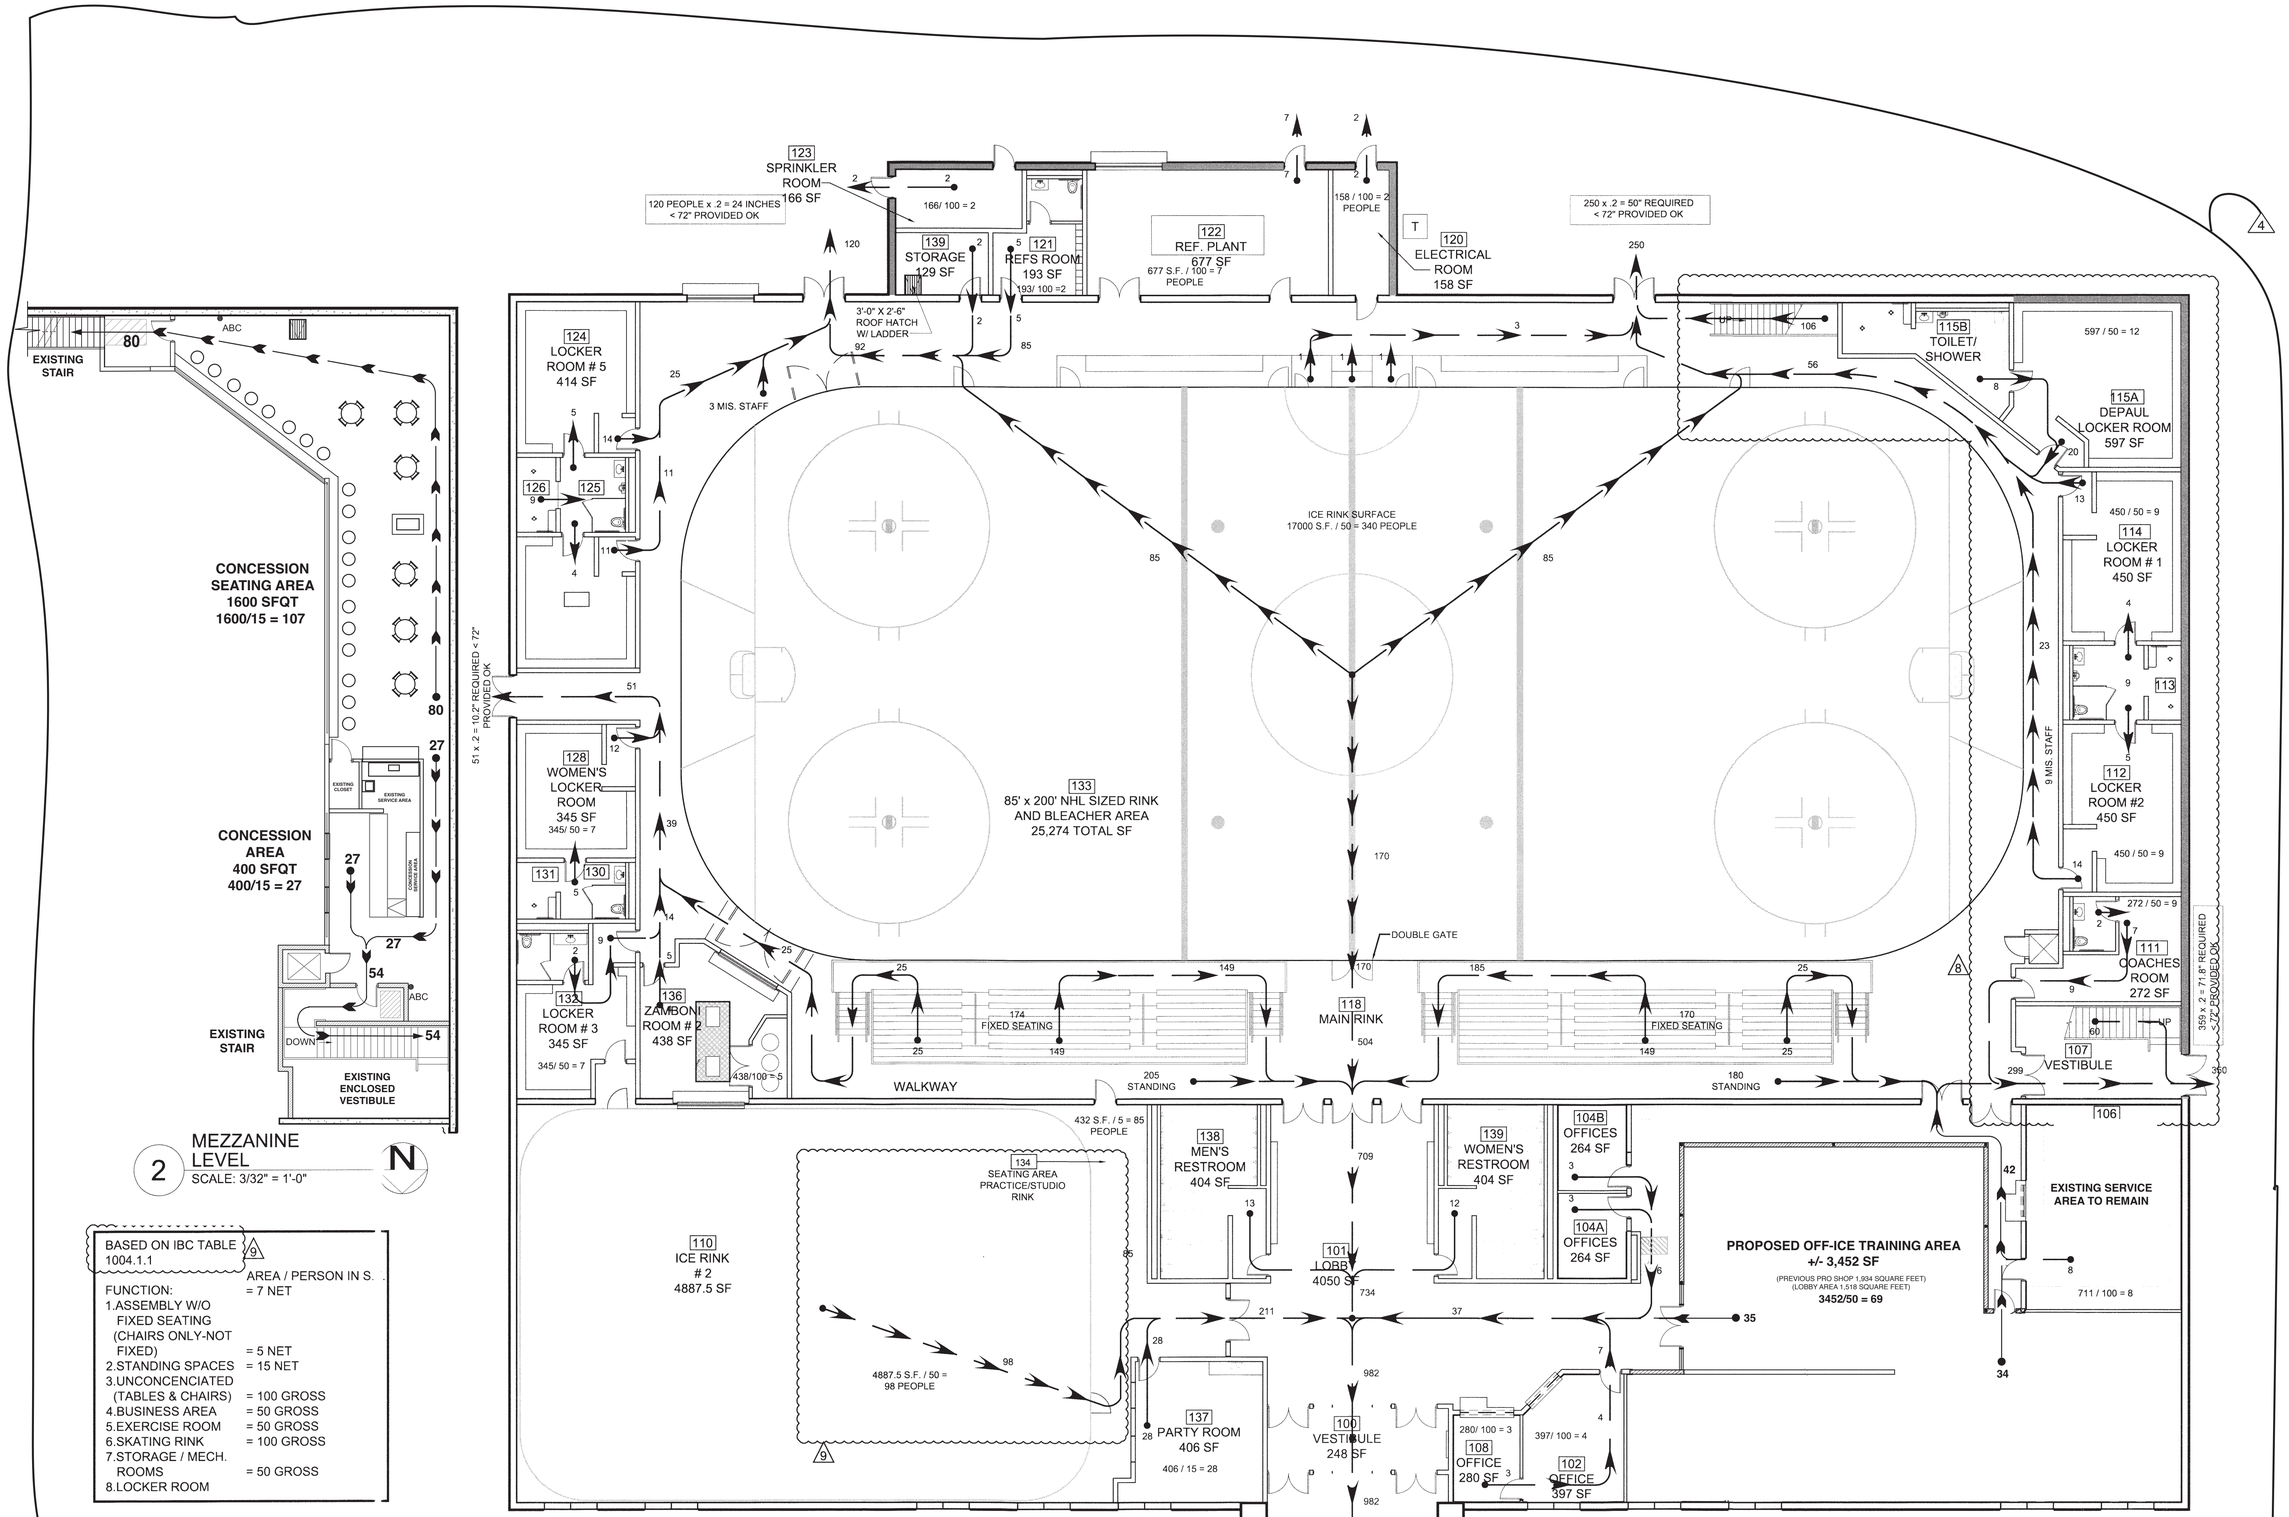

2 MEZZANINE LEVEL
SCALE: 3/32" = 1'-0"

1 GROUND FLOOR PLAN
SCALE: 3/32" = 1'-0"

BASED ON IBC TABLE 1004.1.1 9

FUNCTION:	AREA / PERSON IN S.
1.ASSEMBLY W/O FIXED SEATING (CHAIRS ONLY-NOT FIXED)	= 7 NET = 5 NET
2.STANDING SPACES	= 15 NET
3.UNCONCENCIATED (TABLES & CHAIRS)	= 100 GROSS
4.BUSINESS AREA	= 50 GROSS
5.EXERCISE ROOM	= 50 GROSS
6.SKATING RINK	= 100 GROSS
7.STORAGE / MECH. ROOMS	= 50 GROSS
8.LOCKER ROOM	

VIRGIL JAMES, INC.
+ architecture
+ interiors
+ construction management

321 south jefferson street
chicago, il 60661

VIRGILJAMESINC.COM

All Rights Reserved
OWNERSHIP OF DOCUMENTS

COPYRIGHT
Virgil James, Inc. shall retain all copyrights, statutory and common law right with regard to these plans and design content. Reproduction, changes or assignment to any third party shall not occur without obtaining expressed written permission & consent of Virgil James, Inc.

LIMITATION OF WARRANTY
The Architect and his Consultants do not warrant or guarantee the accuracy and completeness of the work product therein beyond a reasonable diligence. If mistakes, omissions or discrepancies are found to exist within the work product, the Architect shall be promptly notified so that he may have the opportunity to take whatever steps necessary to resolve them. Failure to promptly notify the Architect of such conditions shall absolve the Architect from any responsibility for the consequences of such failure. Actions taken without the knowledge and consent of the Architect, or in contradiction to the Architect's work product or recommendation, shall become the responsibility not of the Architect, but of the parties responsible for taking such actions.

NORTHSHORE ICE ARENA
PARTIAL MEZZANINE + LOBBY RENOVATION
2111 FOUNDERS DRIVE
NORTHBROOK, IL 60062

ISSUED FOR:	DATE:
REV SUBMITTAL	**01.04.2023**
REV 1	**02.06.2023**
REV 2	**05.08.2023**
PERMIT REV SUBMIT	**07.14.2023**
NORTHBROOK REVIEW 4	**08.08.2023**

JOB NUMBER:
TF2620

DRAWN BY:
TE/SE/MB

SHEET NUMBER:

A0.1
Egress Plan